CUADRO DE CONSTRUCCION (PREDIO FISICO)

LADO EST	LADO PV	RUMBO	DISTANCIA	V	COORDENADAS Y	COORDENADAS X
				1	2.281.868.3240	662.474.5001
1	2	S 12 19°33.41" W	35.134	2	2.281.834.0000	662.467.0000
2	3	N 78 55°34.74" W	98.964	3	2.281.853.0081	662.369.8790
3	4	N 11 09°12.15" E	34.687	4	2.281.887.0403	662.376.5888
4	1	S 79 10°41.28" E	99.684	1	2.281.868.3240	662.474.5001

SUPERFICIE = 3,466.938 m2

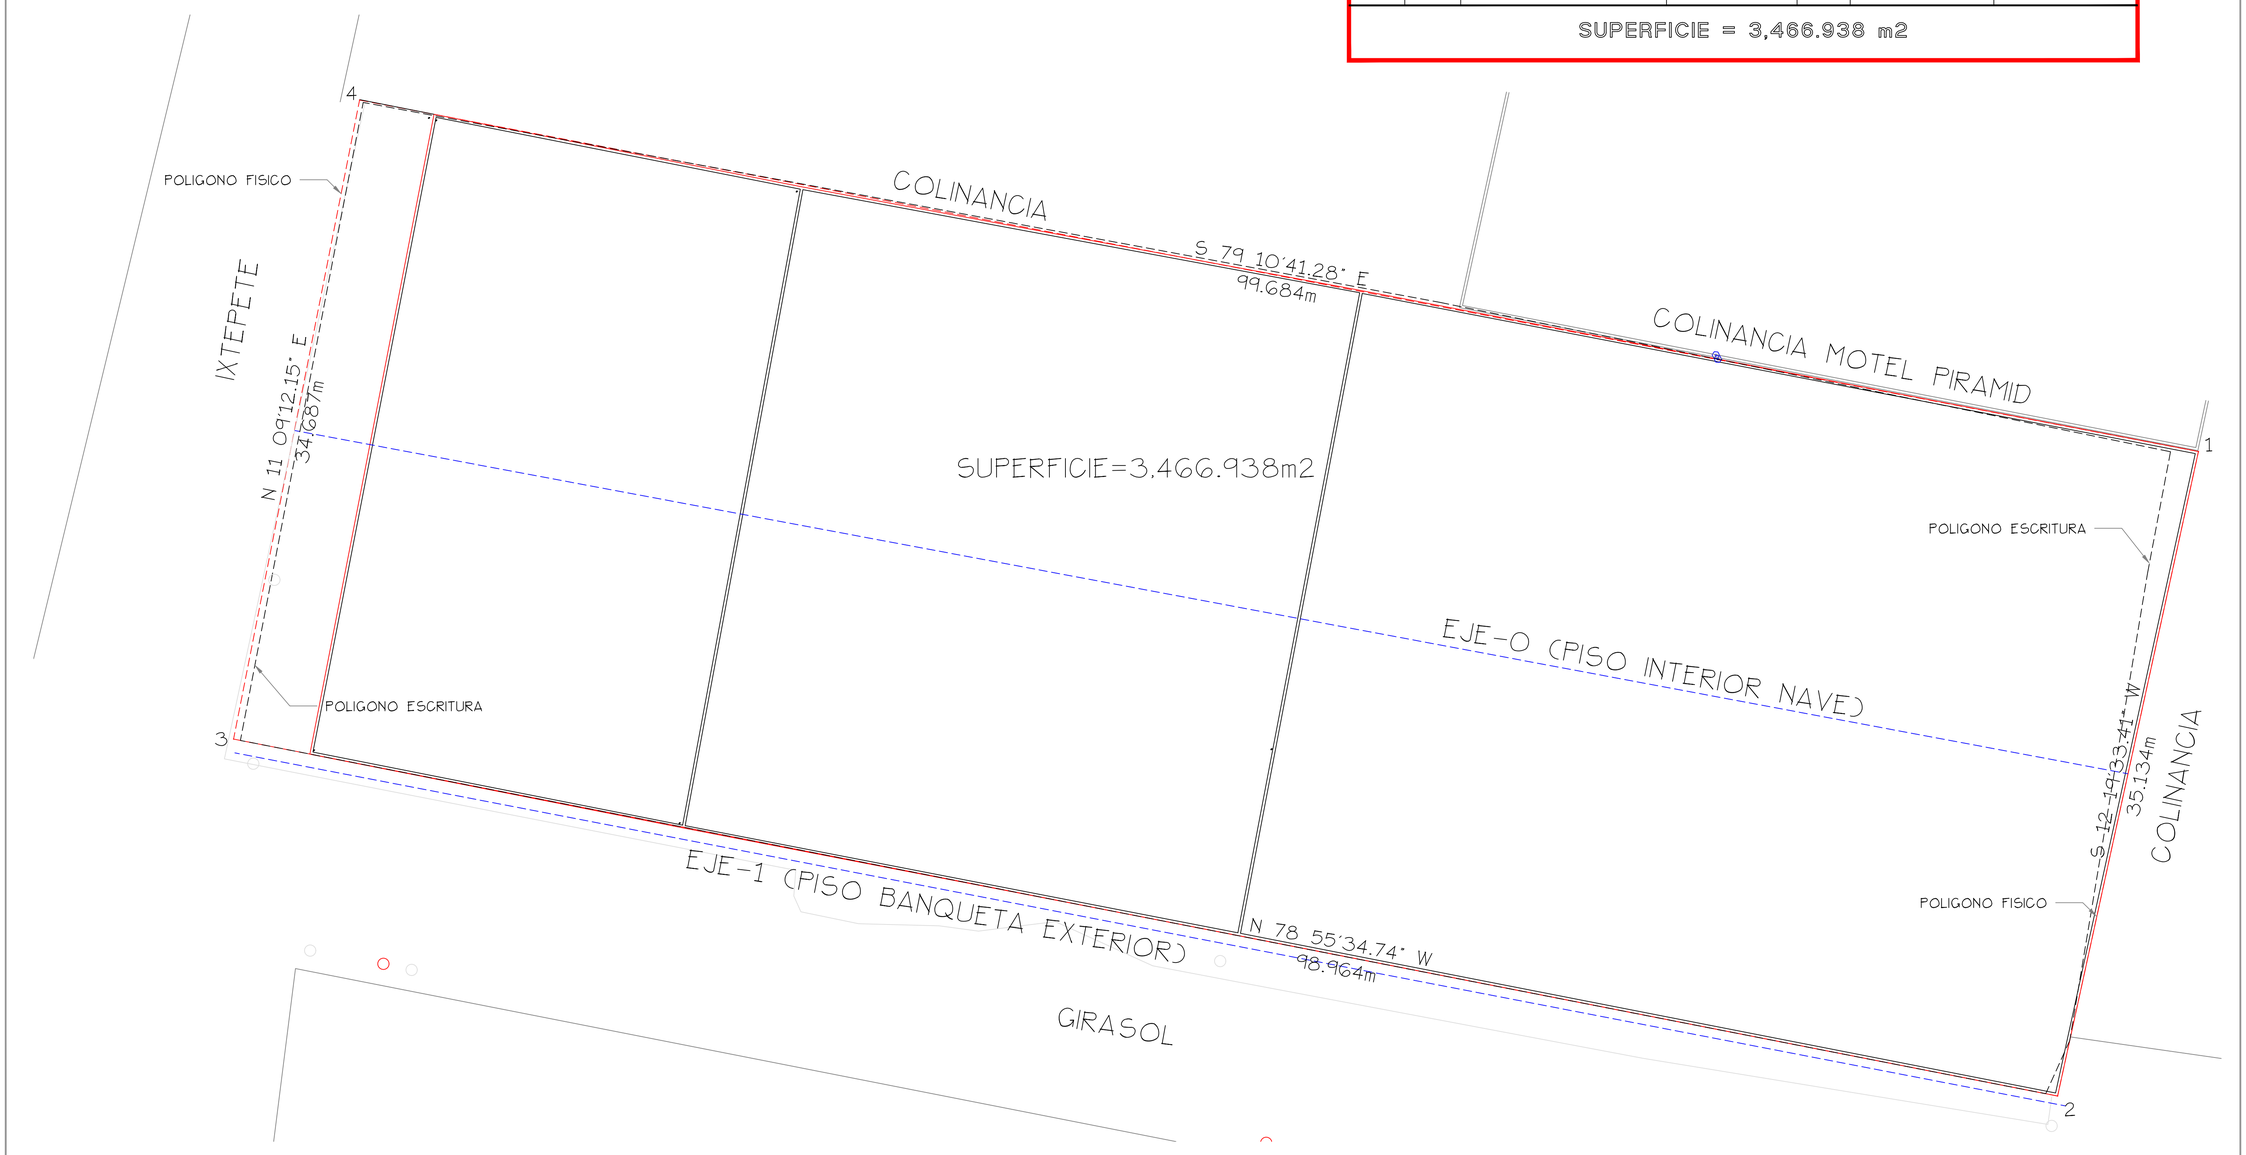

orientación plantas

TITULO DE PROYECTO:
LEVANTAMIENTO TOPOGRÁFICO

Municipio, Estado
ZAPOPAN, JALISCO

UBICACION:

UBICADO: CALLE GIRASOL No.530
COLONIA MARIANO OTERO
ZAPOPAN, JALISCO

SIMBOLOGÍA
- POSTE CFE
- POSTE TELMEX

Coordenadas:
ITRF2008 / UTM zona 13
GGM10 altura

contiene
- POLIGONAL EXISTENTE
- PLANO ESCRITURA DIGITALIZADA
- CUADRO DE CONSTRUCCIÓN

cliente:
Ing. Héctor Lopéz

ejecutó:
ING. CRISTÓBAL ROMERO IBARRA
ING. ISAAC E. LOZA SALCEDO

nombre de archivo:
Mariano Otero.dwg

responsable:

acotación	escala
Mts.	1 : 150

CR77 TOPOGRAFÍA

Plano
1 de 2

fecha
25/SEPTIEMBRE/2023